

PODROBNÝ PODELNÝ PROFIL: SO 161
M 1:1000/100
ROZSAH: KM 0,15609 – 0,96680
Druh povrchu území:
katastrální území:
okres:
Kraj:


TRVALÝ TRAVNÍ POROST
OSTATNÍ PLOCHA
ORNÁ PŮDA
HOBNÍ ZOAR
BRUSNICE

ORNÁ PŮDA

TRUTNOV
KRALOVÉHRADSKÝ

LESNÍ POZEMEK

OSTATNÍ PLOCHA

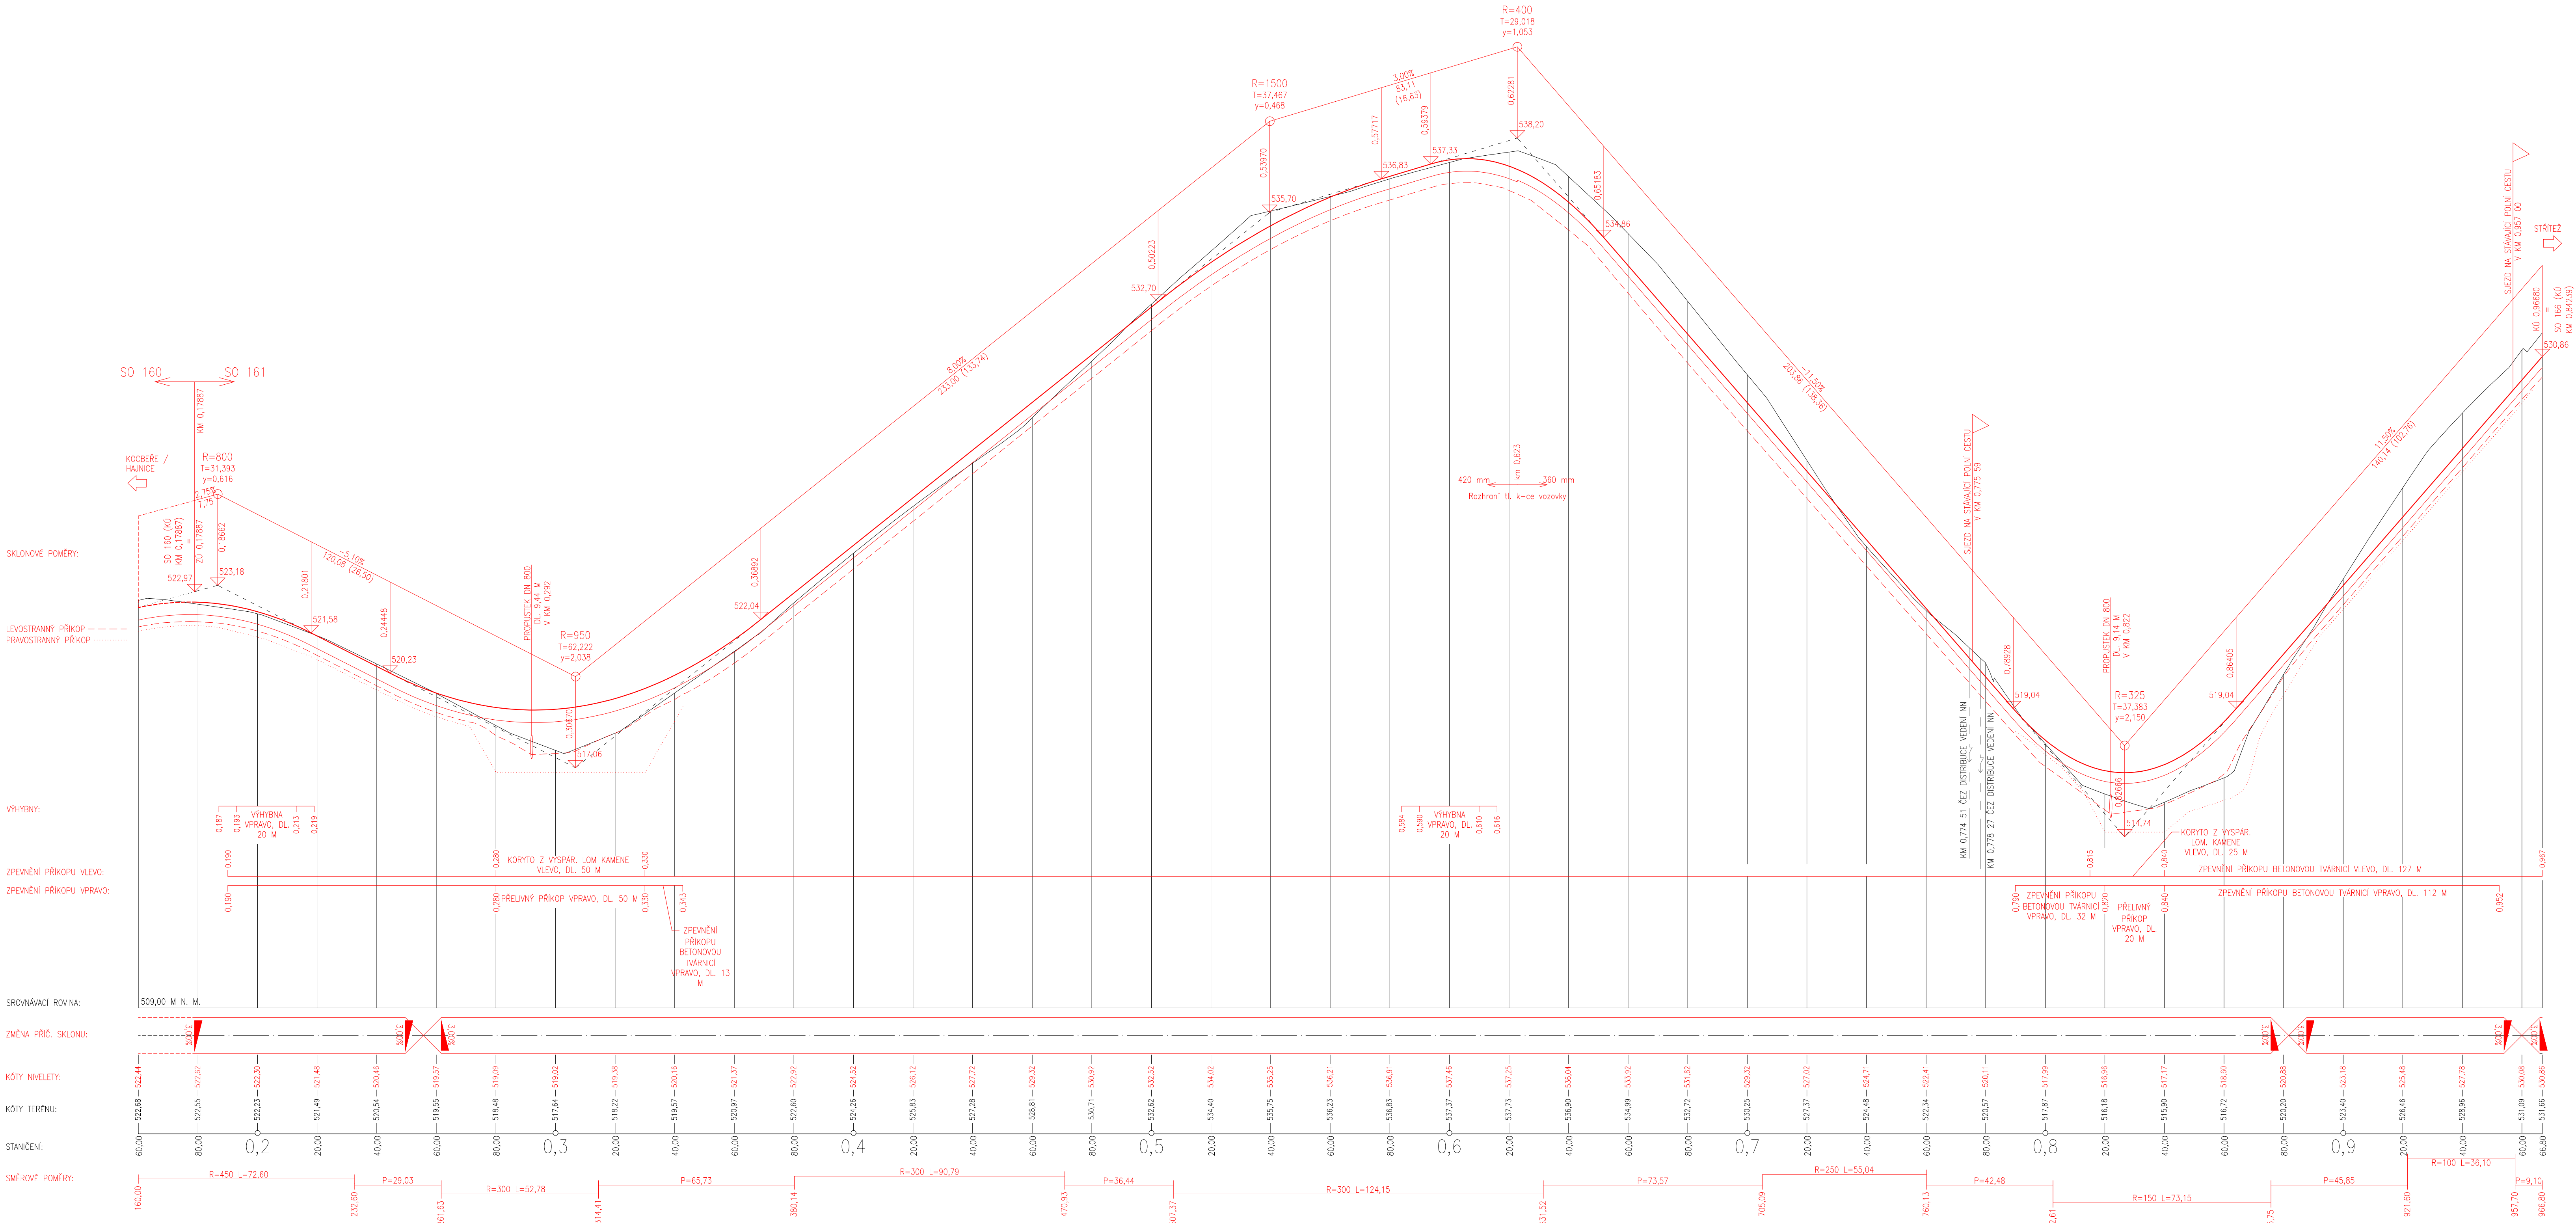

SO 161 D.1.1

VÝŠKOVÝ SYSTÉM BpV SOUŘADNICOVÝ SYSTÉM S-JTSK

Číslo změny:	Obsah změny:	Datum změny:
01	-	-
02	-	-
03	-	-

Objednatel: 	Ředitelství silnic a dálnic s. p. Na Pankraci 546/56, 140 00 Praha 4 Stavbu zajišťuje Závod Praha Na Pankraci 546/56, 140 00 Praha 4
------------------------	--

Zhotovitel: Společnosti ve sdružení SUDOP PRAHA a.s. Hlavní inženýr projektu: Ing. Roman Petřík	SG_Velké projekty, BIM 2020 zastoupené Olšanská 1a, 130 80 Praha 3 telefon: +420 267 094 111
--	--

--	--	--	--	--

Spolupráce: 	SUDOP PRAHA a.s. Olšanská 1a, 130 80 Praha 3 tel.: +420 267 094 111 e-mail: praha@sudop.cz	Vedoucí týmu: ING. ROMAN PETŘÍK	Asistent vedoucího týmu: ING. PAVEL MICHL Specializace profese: -
------------------------	---	---	---

Zpracovatel: 	projektová, průzkumná a konzultační společnost PUDIS a.s., Podbabská 1014/20, 160 00 Praha 6 tel.: +420 267 004 111, www.pudis.cz, info@pudis.cz
-------------------------	---

Vedoucí oddělení: ING. ZDENĚKA BOLEHOVSKÁ	Odpovědný projektant SO, KO, PS: ING. MICHAL TUREK	Vypracoval: ING. TOMÁŠ VÁŇA	Kontroloval: ING. MICHAL TUREK
---	--	---------------------------------------	--

Název akce: D11 1108 Jaroměř - Trutnov VD-ZDS + TP + AD	Číslo směrnice: 22-014.250
Část: D.1.1 OBJEKTY POZEMNÍCH KOMUNIKACÍ VČETNĚ PROPUSTKŮ SO 161 PŘÍSTUPY NA POZEMKY V K.Ú BRUSNICE	Projektový stupeň: VD-ZDS
Název přílohy: PODELNÝ PROFIL	Datum: 11/2024
	Číslo část: D.1.1
	Měřítko: 1:1000/100
	Formát: 12x44
	Číslo přílohy: 3

DOKUMENT LZE UŽÍVAT POUZE VE SMYSLU PŘEDLOŽENÉHO ÚČELU. ŽÁDNÁ JINÁ ČÁST NEJDE UŽÍVAT JINAK NEŽ JE UČELNĚ ZAMÝŠLENÁ. KOPÍROVÁNÍ NEBO JINÝ ZPŮSOB NEDOPORUČUJEME. BEZ SOUHLASU SUDOP PRAHA A.S.