

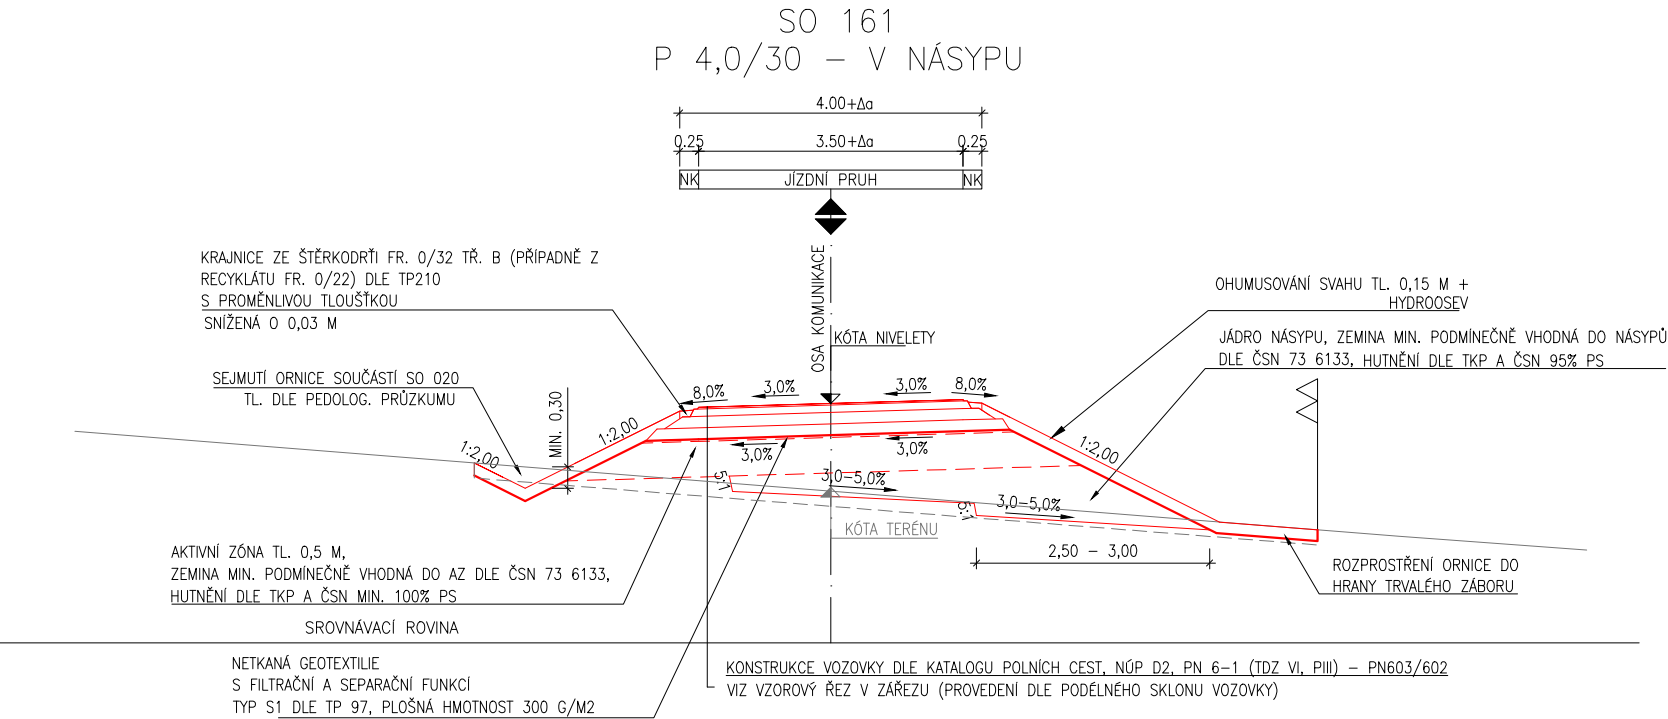


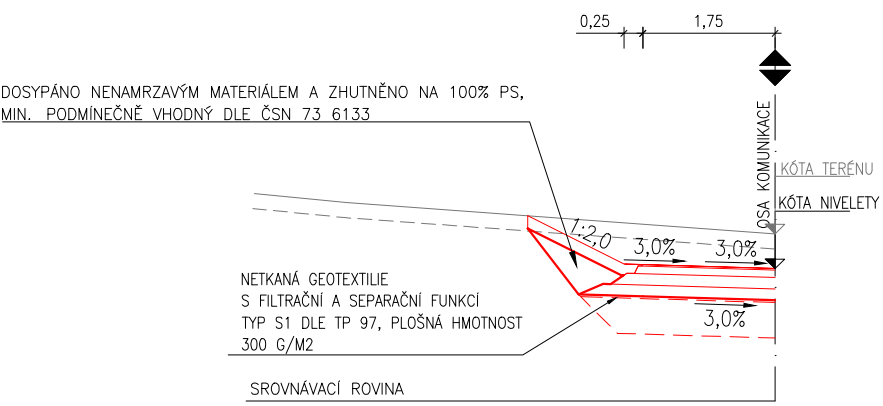

SO 161
P 4,0/30 – V ŽÁŘEZU BEZ PŘÍKOPU

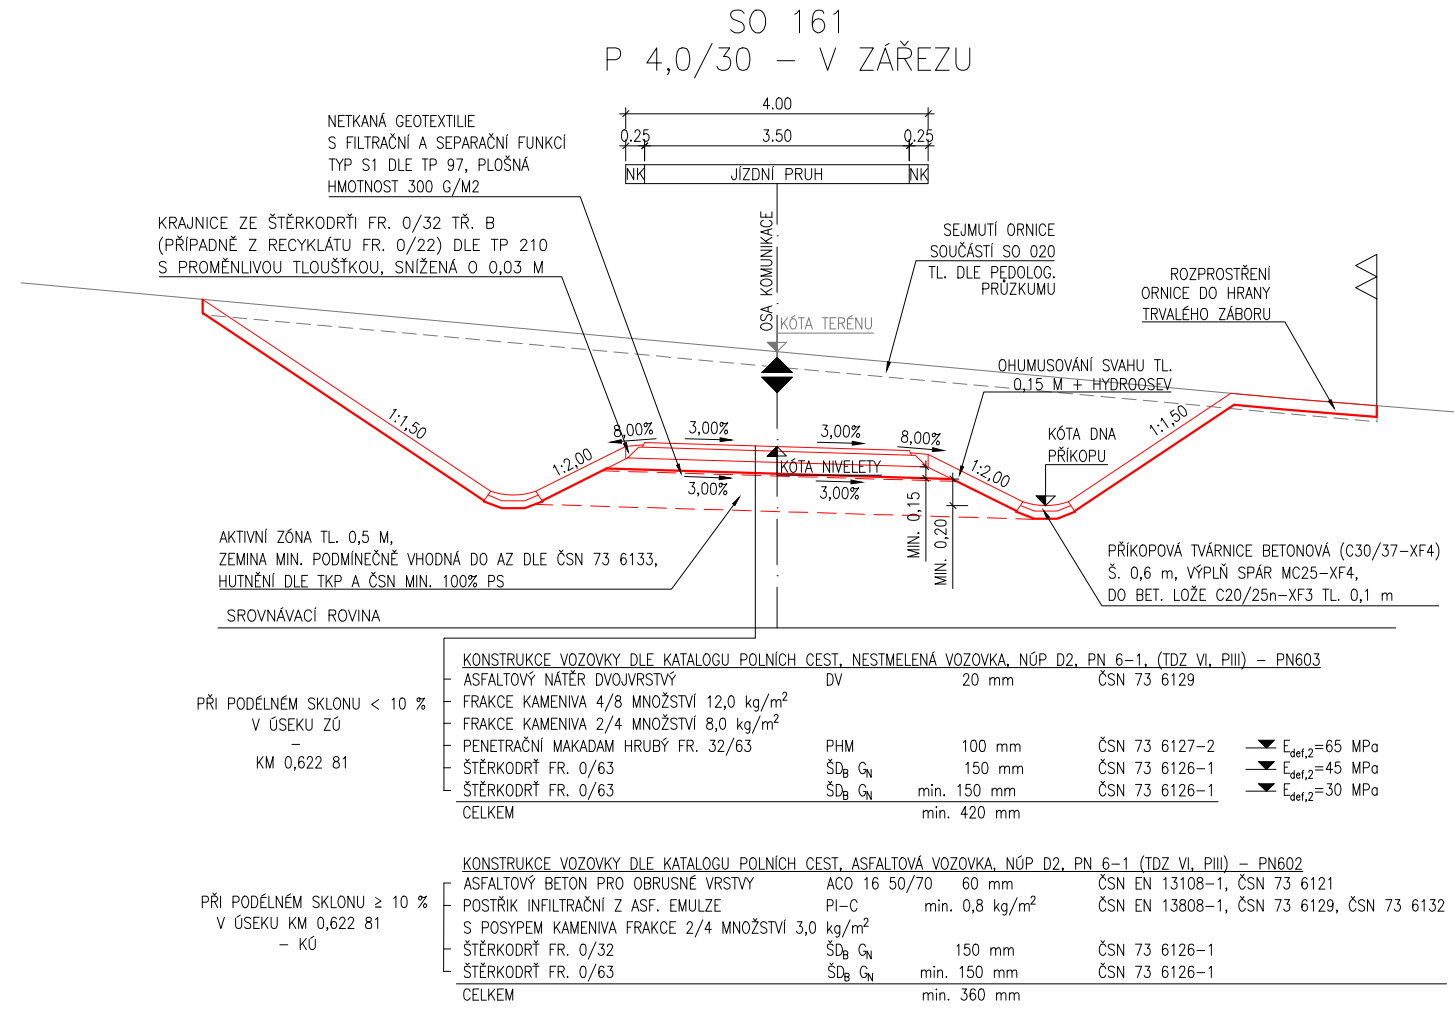

SO 161 D.1.1

VÝŠKOVÝ SYSTÉM Bpv SOUŘADNICOVÝ SYSTÉM S-JTSK

Číslo změny:	Obsah změny:	Datum změny:
01	-	-
02	-	-
03	-	-



**ŘEDITELSTVÍ
SILNIC
A DÁLNIC**

Ředitelství silnic a dálnic s. p.
Na Pankráci 546/56, 140 00 Praha 4

Stavbu zajišťuje Závod Praha
Na Pankráci 546/56, 140 00 Praha 4

Zhotovitel: Společníci ve sdružení

SG_Velké projekty_BIM 2020
zastoupené

SUDOP PRAHA a.s.
Hlavní inženýr projektu: Ing. Roman Petřík

Olšanská 1a, 130 80 Praha 3
telefon: +420 267 094 111



Správce:  SUDOP PRAHA a.s. Olšanská 1a, 130 80 Praha 3 tel.: +420 267 094 111 e-mail: praha@sudop.cz	Vedoucí týmu: ING. ROMAN PETŘÍK	Asistent vedoucího týmu: ING. PAVEL MICHL Specialista profese: -
---	---	---

Zpracovatel částí:


projektová, průzkumná a konzultační společnost
PUDIS a.s., Podbabská 1014/20, 160 00 Praha 6
tel.: +420 267 004 111, www.pudis.cz, info@pudis.cz

Vedoucí střediska: ING. ZDEŇKA BOLEHOVSKÁ	Odpovědný projektant SO, IO, PS: ING. MICHAL TUREK	Vypracoval: ING. TOMÁŠ VÁŇA	Kontroloval: ING. MICHAL TUREK
---	--	---------------------------------------	--

Název akce:	Číslo smlouvy: 22-014.250	
D11 1108 Jaroměř - Trutnov VD-ZDS + TP + AD	Projektový stupeň: VD-ZDS	
Část:	Datum: 11/2024	
D.1.1 OBJEKTY POZEMNÍCH KOMUNIKACÍ VČETNĚ PROPUSTKŮ SO 161 PŘÍSTUPY NA POZEMKY V K.Ú BRUSNICE	Číslo části: D.1.1	
Název přílohy:	Měřítko: 1:100	Počet formátů: 3xA4
VZOROVÝ PŘÍČNÝ ŘEZ	Číslo přílohy: 4	