

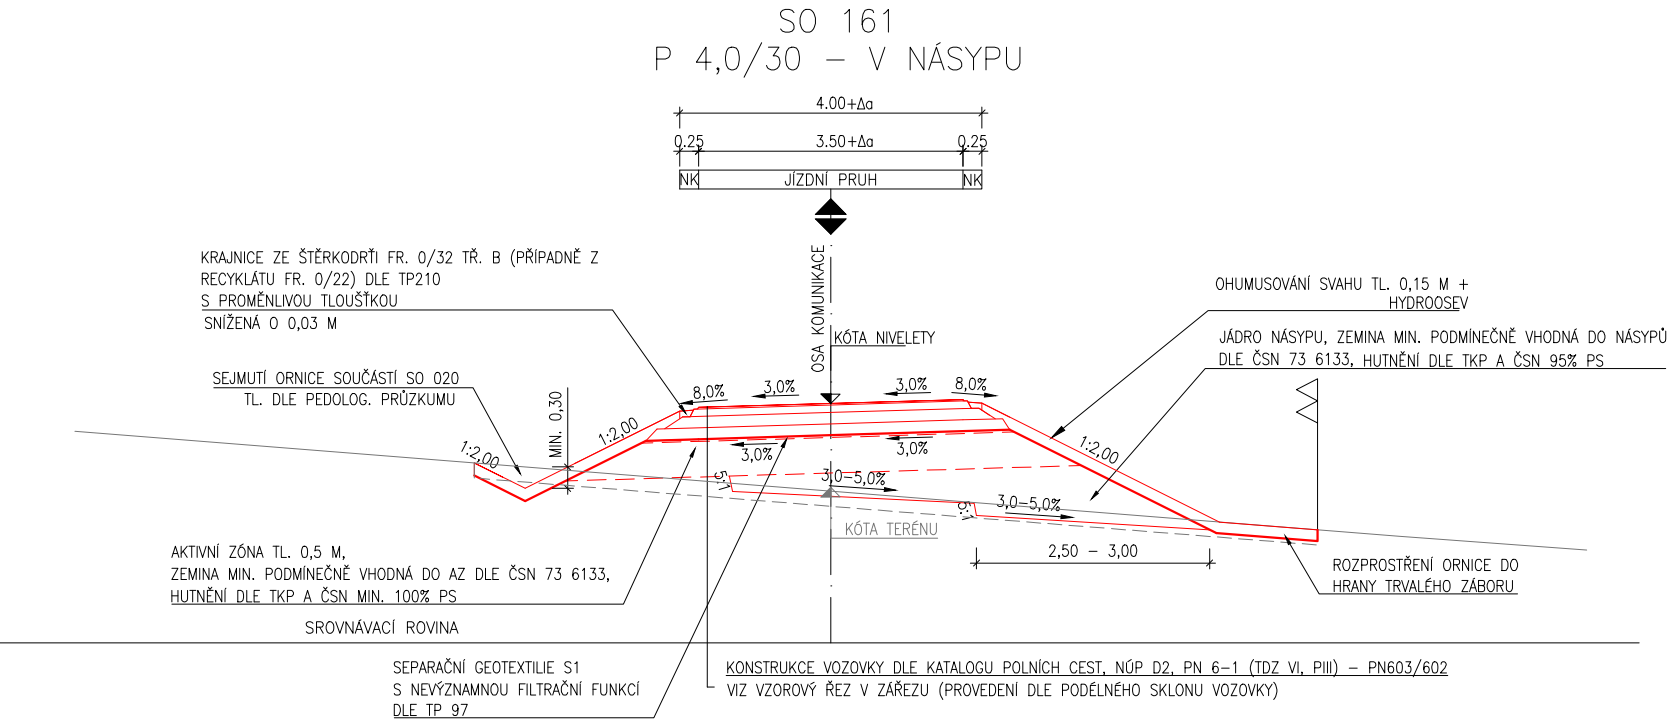


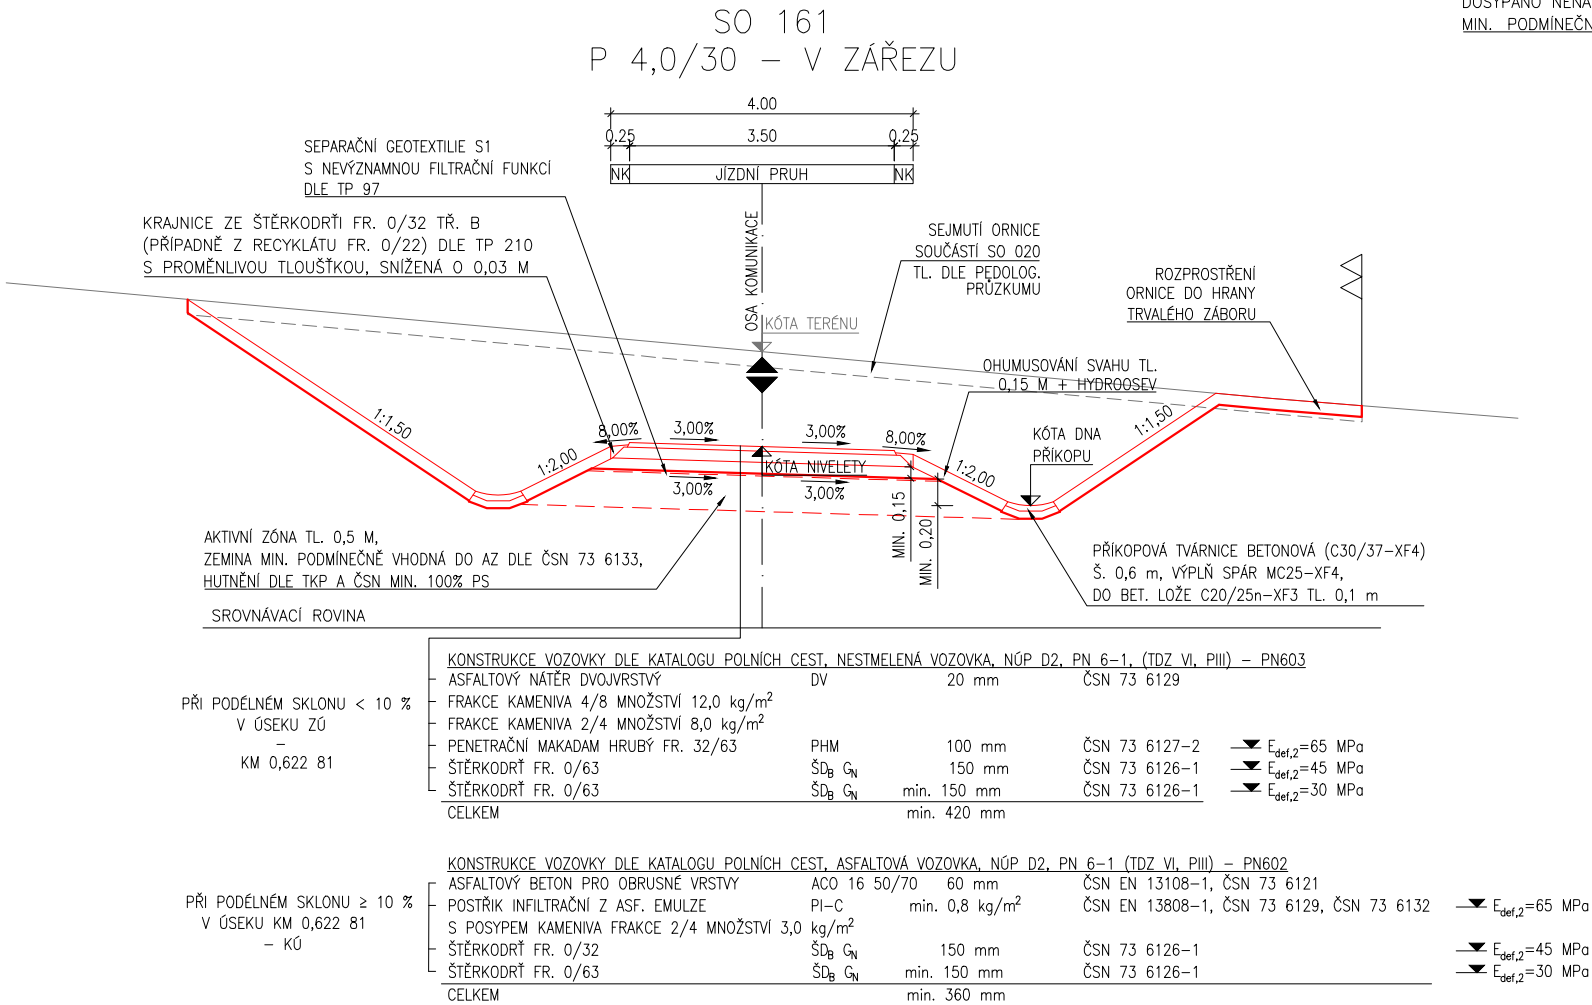

SO 161
P 4,0/30 – V ŽÁŘEZU BEZ PŘÍKOPU

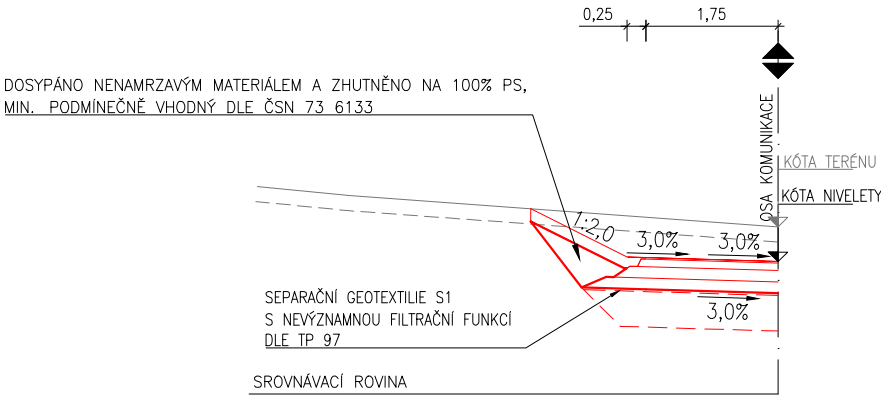

SO 161

D.1.1

VÝŠKOVÝ SYSTÉM Bpv SOUŘADNICOVÝ SYSTÉM S-JTSK

Číslo změny:	Obsah změny:	Datum změny:
01	-	-
02	-	-
03	-	-

Objednatel:



ŘEDITELSTVÍ SILNIC A DÁLNIC

Ředitelství silnic a dálnic s. p.
Na Pankráci 546/56, 140 00 Praha 4

Stavbu zajišťuje Závod Praha
Na Pankráci 546/56, 140 00 Praha 4

Zhotovitel: Společníci ve sdružení

SG_Velké projekty_BIM 2020
zastoupené

SUDOP PRAHA a.s.
Hlavní inženýr projektu: Ing. Roman Petřík

Olšanská 1a, 130 80 Praha 3
telefon: +420 267 094 111



Správce:	SUDOP PRAHA a.s. Olšanská 1a, 130 80 Praha 3 tel.: +420 267 094 111 e-mail: praha@sudop.cz	Vedoucí týmu:	ING. ROMAN PETŘÍK	Asistent vedoucího týmu:	ING. PAVEL MICHL
				Specialista profese:	-

Zpracovatel částí:



projektová, průzkumná a konzultační společnost

PUDIS a.s., Podbabská 1014/20, 160 00 Praha 6
tel.: +420 267 004 111, www.pudis.cz, info@pudis.cz

Vedoucí střediska:	ING. ZDEŇKA BOLEHOVSKÁ	Odpovědný projektant SO, IO, PS:	ING. MICHAL TUREK	Vypracoval:	ING. TOMÁŠ VÁŇA	Kontroloval:	ING. MICHAL TUREK
---------------------------	------------------------	---	-------------------	--------------------	-----------------	---------------------	-------------------

Název akce:	D11 1108 Jaroměř - Trutnov VD-ZDS + TP + AD		Číslo smlouvy:	22-014.250	
			Projektový stupeň:	VD-ZDS	
Část:	D.1.1 OBJEKTY POZEMNÍCH KOMUNIKACÍ VČETNĚ PROPUSTKŮ SO 161 PŘÍSTUPY NA POZEMKY V K.Ú BRUSNICE		Datum:	11/2024	
			Číslo části:	D.1.1	
Název přílohy:	VZOROVÝ PŘÍČNÝ ŘEZ		Měřítko:	1:100	Počet formátů: 3xA4
			Číslo přílohy:	4	