

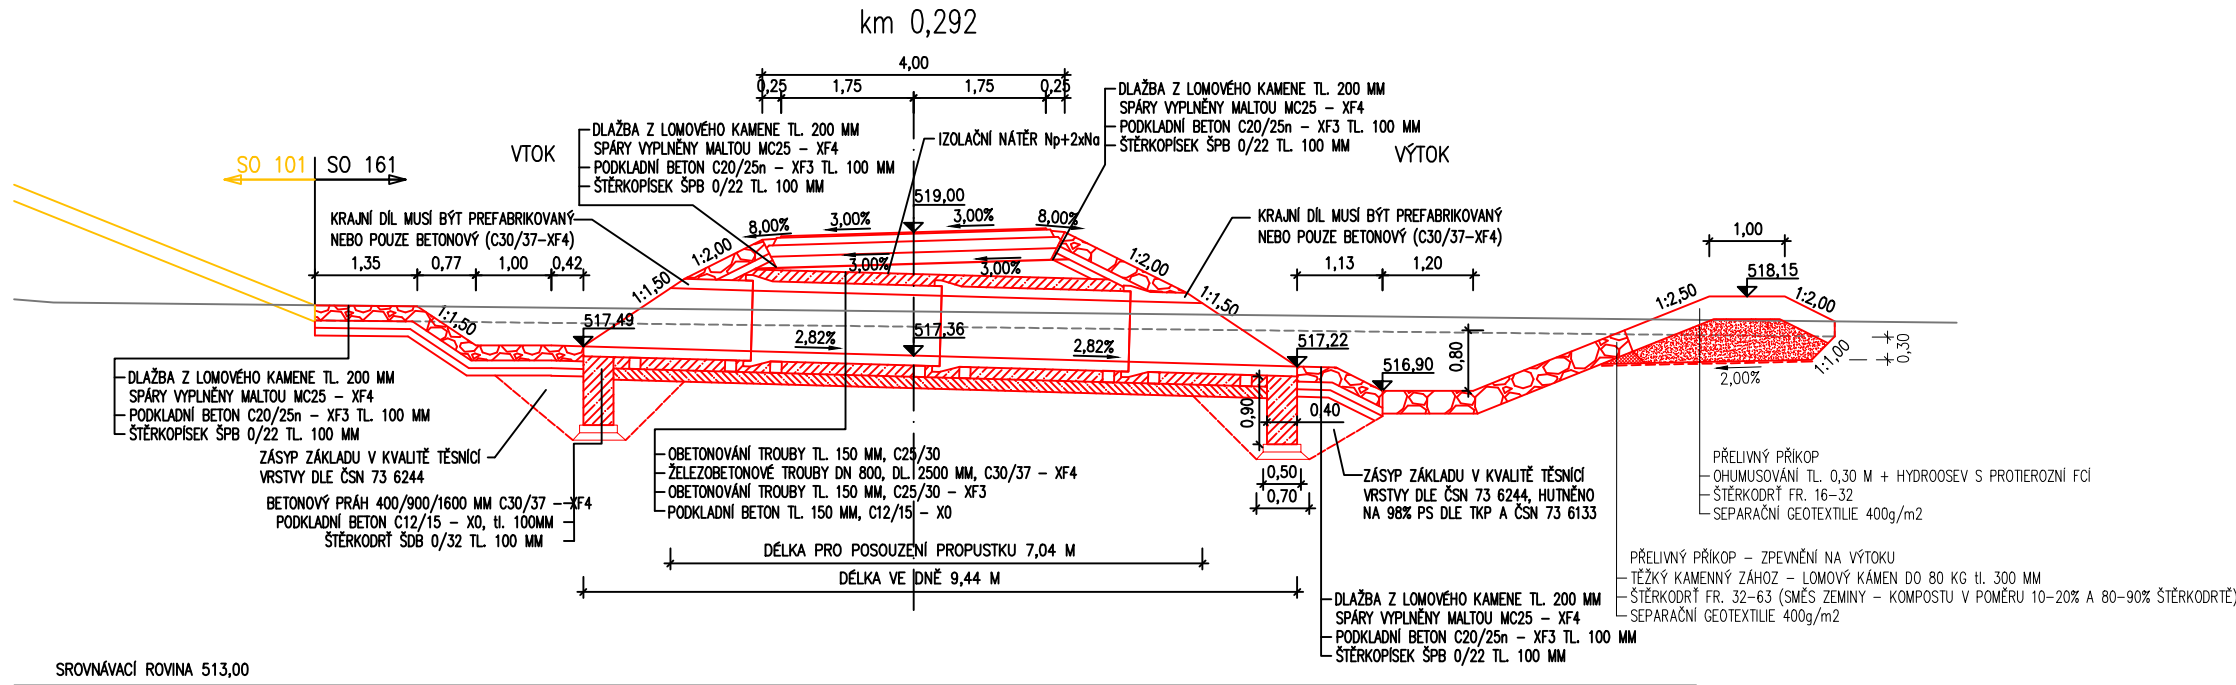



km 0,292
DN 800
PŮDORYS PROPUSTKU (M 1:100)

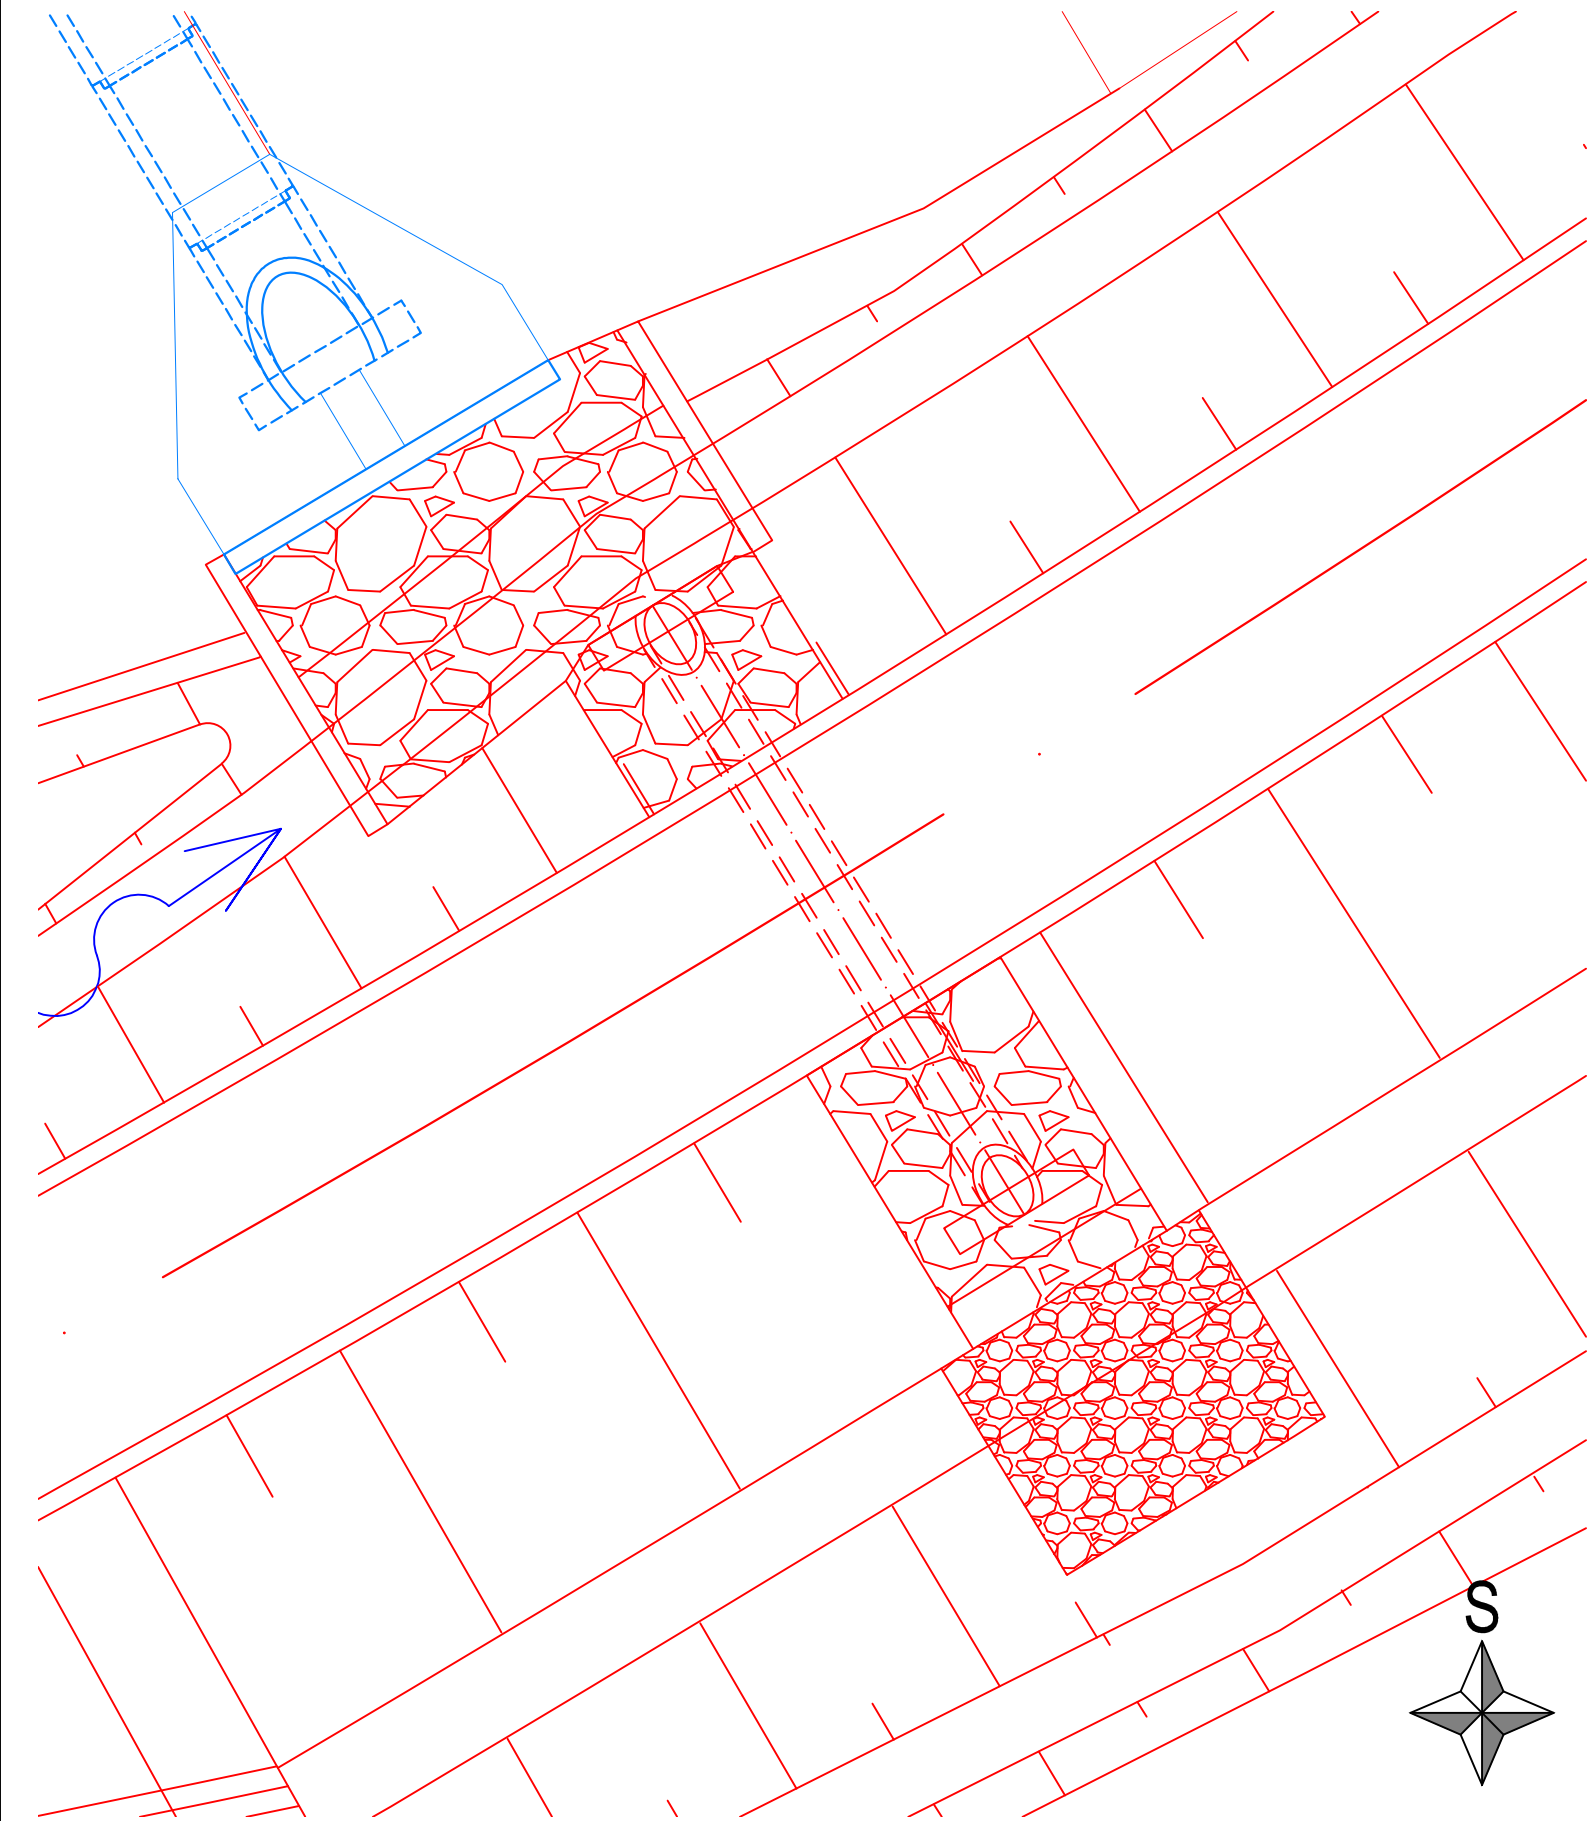


PŘÍČNÝ ŘEZ ULOŽENÍM PROPUSTKU
POD KOMUNIKACÍ

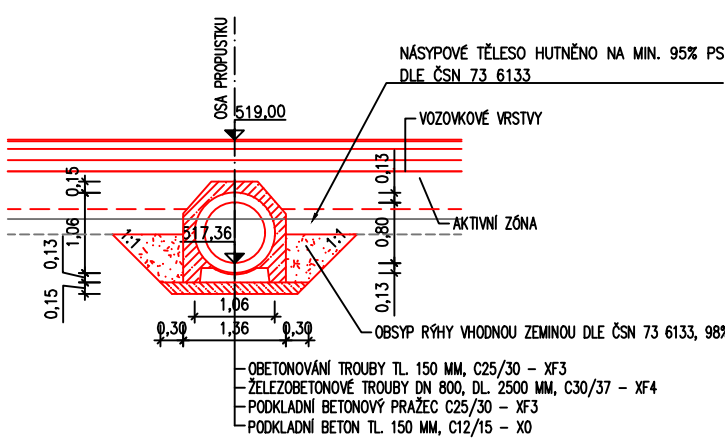


PŘELIVNÝ PŘÍKOP
KONSTRUKCE NA VÝTOKU
(V DÉLCE 2 M OD OSY PROPUSTKU)

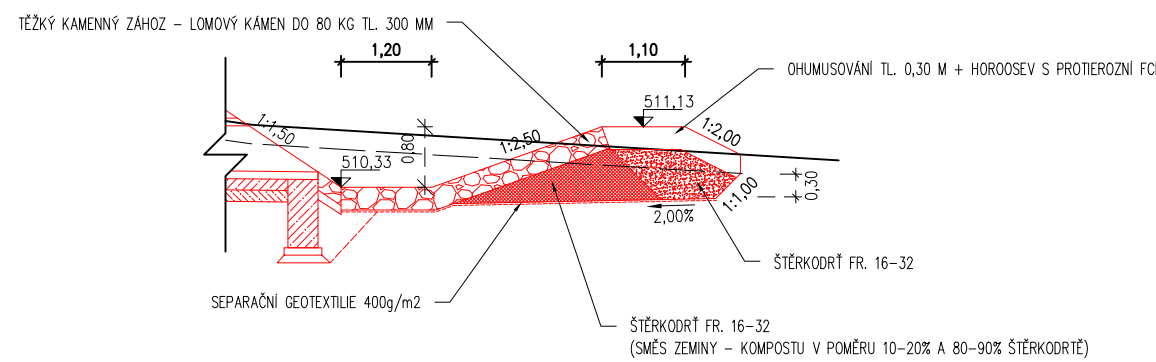

PŘELIVNÝ PŘÍKOP
KONSTRUKCE ZA VÝTOKEM
(V DÉLCE 2 M OD KONST. NA VÝTOKU)

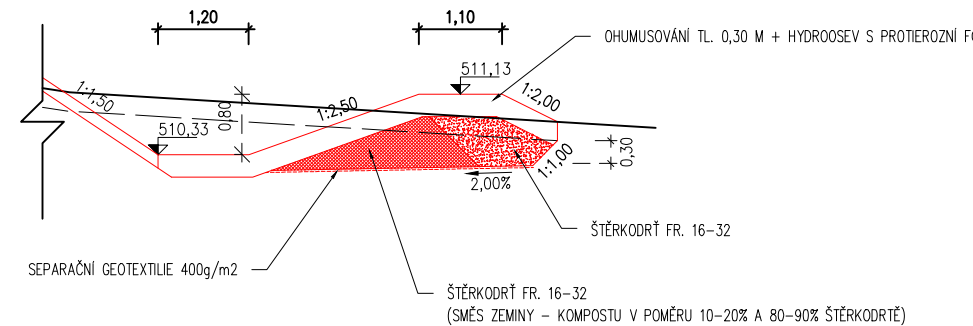

PŘELIVNÝ PŘÍKOP
STANDARDNÍ KONSTRUKCE
(NA ZBYLÝCH ÚSECÍCH PŘÍKOPU)

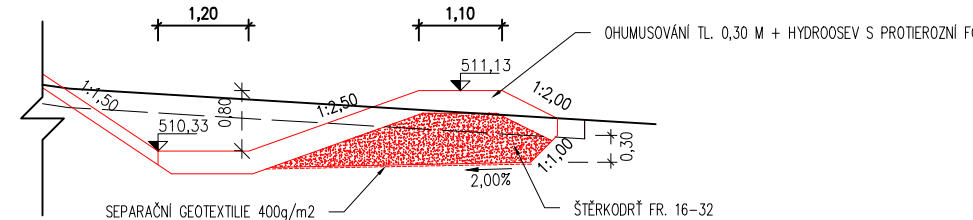

SO 161 D.1.1

VÝŠKOVÝ SYSTÉM BpV

SOUŘADNICOVÝ SYSTÉM S-JTSK

Číslo změny:	Obsah změny:	Datum změny:
01	-	-
02	-	-
03	-	-

Objednatel:	Ředitelství silnic a dálnic s. p. Na Pankráci 546/56, 140 00 Praha 4
	Stavbu zajišťuje Závod Praha Na Pankráci 546/56, 140 00 Praha 4

Zhotovitel: Společníci ve sdružení	SG_Velké projekty BIM 2020 zastoupené
SUDOP PRAHA a.s. Hlavní inženýr projektu: Ing. Roman Petřík	Olšanská 1a, 130 80 Praha 3 telefon: +420 267 094 111

--	--	--	--	--

Správce:	SUDOP PRAHA a.s. Olšanská 1a, 130 80 Praha 3 tel.: +420 267 094 111 e-mail: praha@sudop.cz	Vedoucí týmu:	Asistent vedoucího týmu:
		ING. ROMAN PETŘÍK	ING. PAVEL MICHL Specialista profese:

Zpracovatel částí:	projektová, průzkumná a konzultační společnost PUDIS a.s., Podbabská 1014/20, 160 00 Praha 6 tel.: +420 267 004 111, www.pudis.cz, info@pudis.cz
--------------------	--

Vedoucí střediska:	Odpovědný projektant SO, IO, PS:	Vypracoval:	Kontroloval:
ING. ZDEŇKA BOLEHOVSKÁ	ING. MICHAL TUREK	ING. TOMÁŠ VÁŇA	ING. MICHAL TUREK

Název akce:	Číslo smlouvy:
D11 1108 Jaroměř - Trutnov VD-ZDS + TP + AD	22-014.250
Část:	Projektový stupeň:
D.1.1 OBJEKTY POZEMNÍCH KOMUNIKACÍ VČETNĚ PROPUSTKŮ SO 161 PŘÍSTUPY NA POZEMKY V K.Ú BRUSNICE	VD-ZDS
Název přílohy:	Datum:
PROPUSTEK DN 800 V KM 0,292	11/2024
	Číslo části:
	D.1.1
	Měřítko:
	1:100
	Počet formátů:
	4xA4
	Číslo přílohy:
	6.1

DOKUMENT LZE UŽÍVAT POUZE VE SMYSLU PŘÍSLUŠNÉ SMLOUVY O DÍLO. ŽÁDNÁ JEHO ČÁST NEMŮŽE BYT DLE ZÁKONA č. 121/2000 Sb. KOPIROVÁNA NEBO JINÝM ZPŮSOBEM ROZŠÍŘOVÁNA. BEZ SOUHLASU SUDOP PRAHA a.s.