
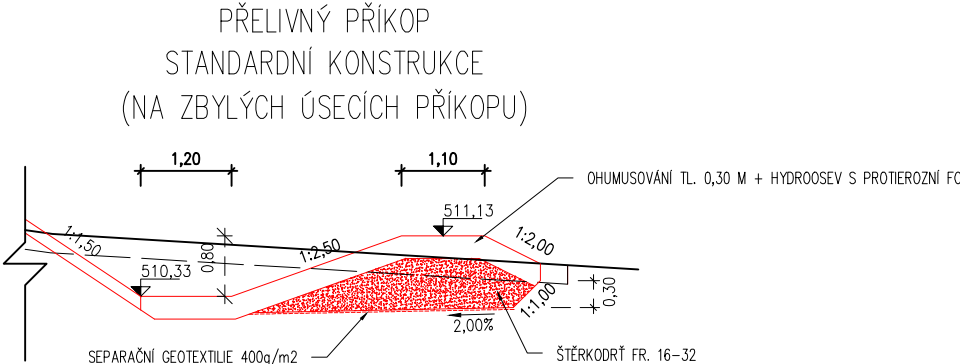
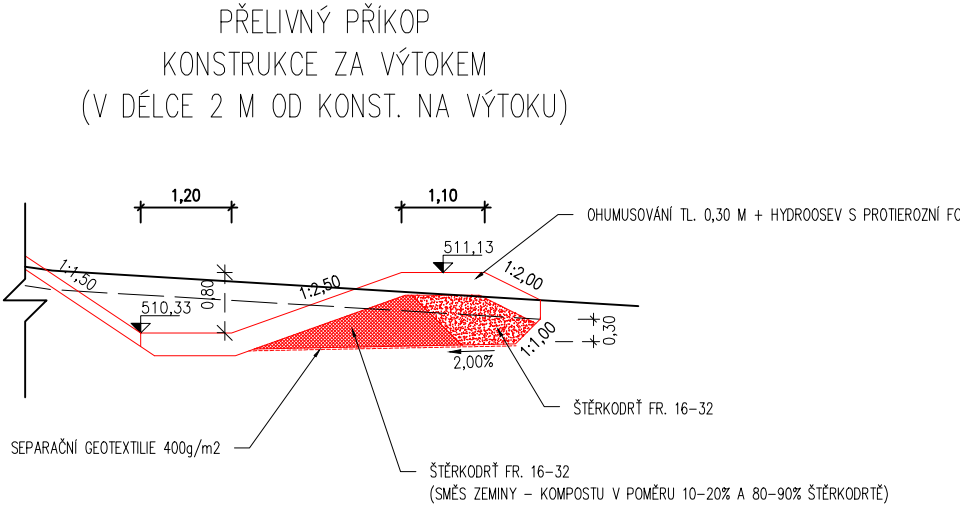
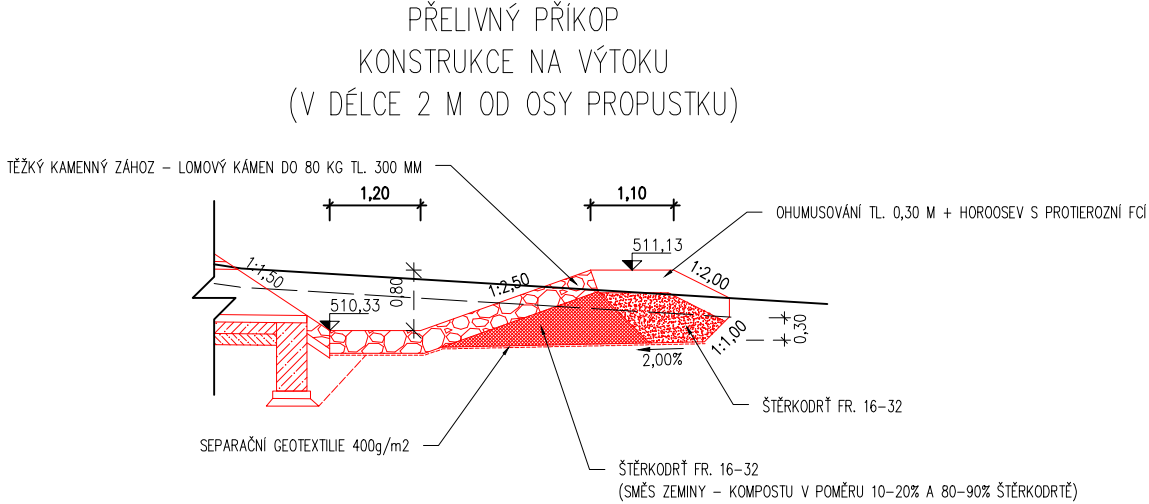
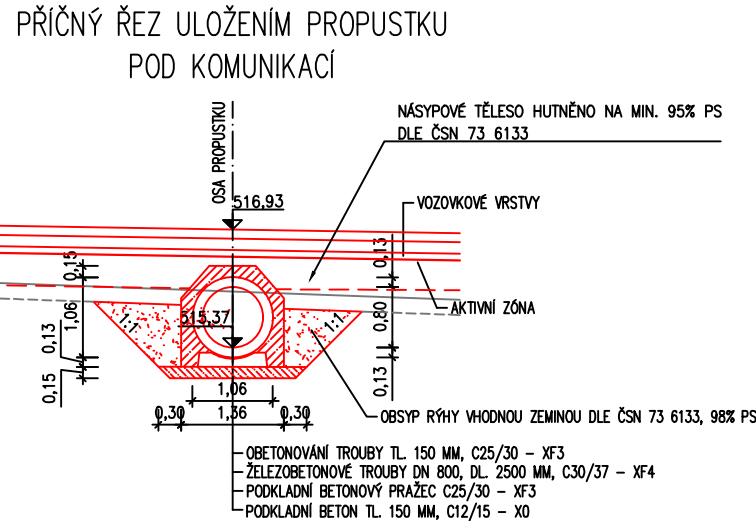
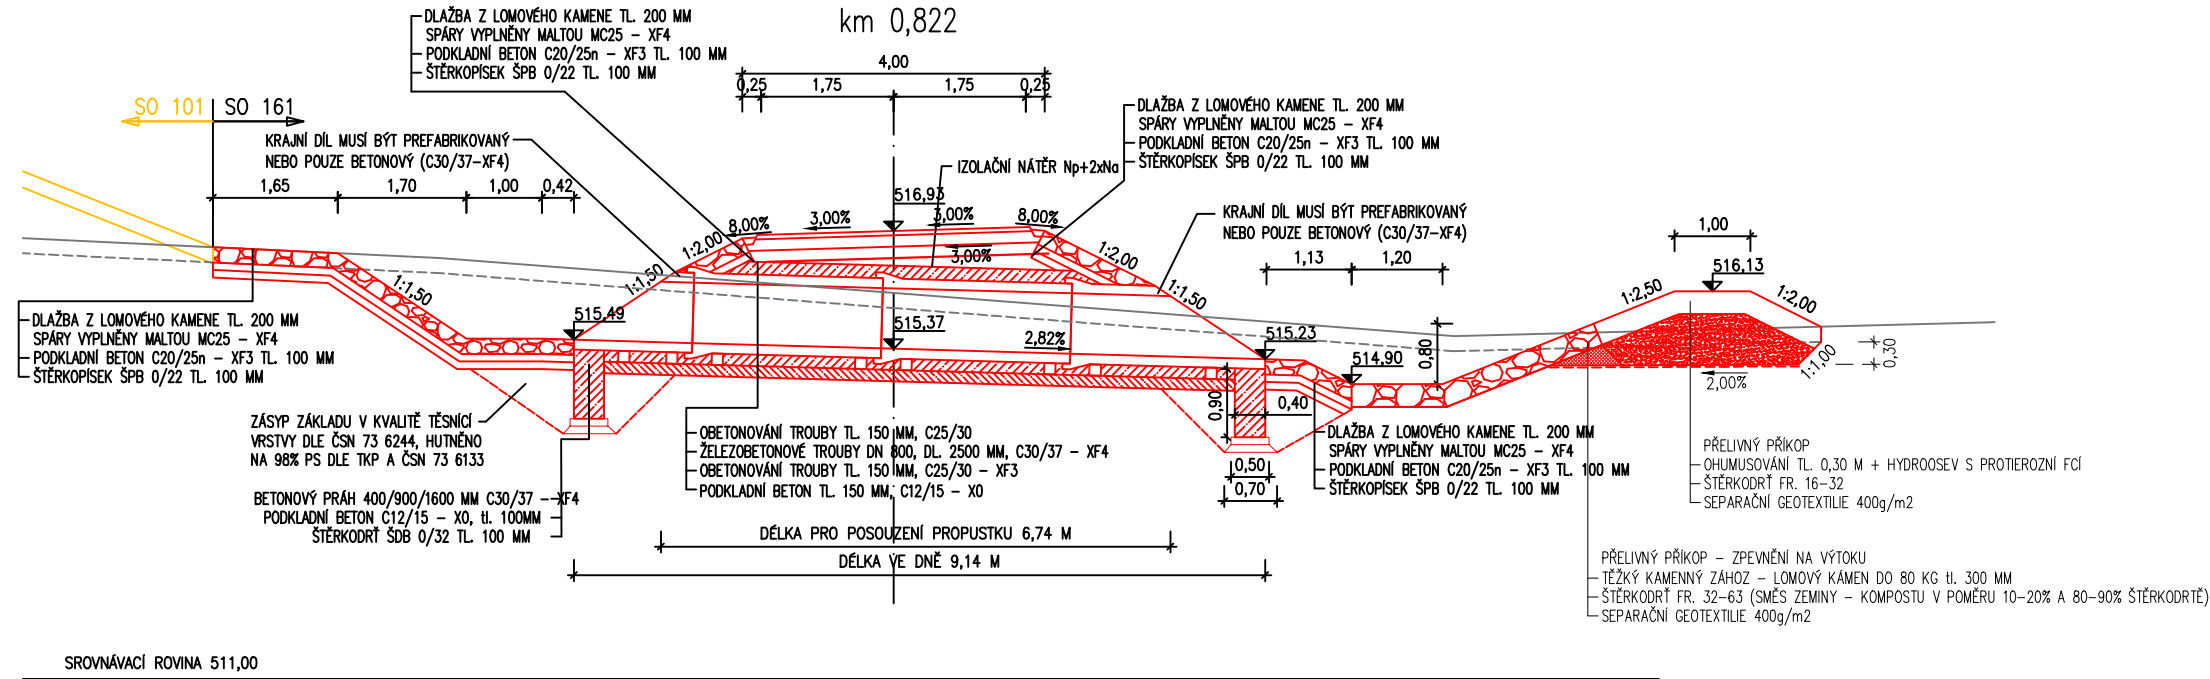


km 0,822
DN 800
PŮDORYS PROPUSTKU (M 1:100)

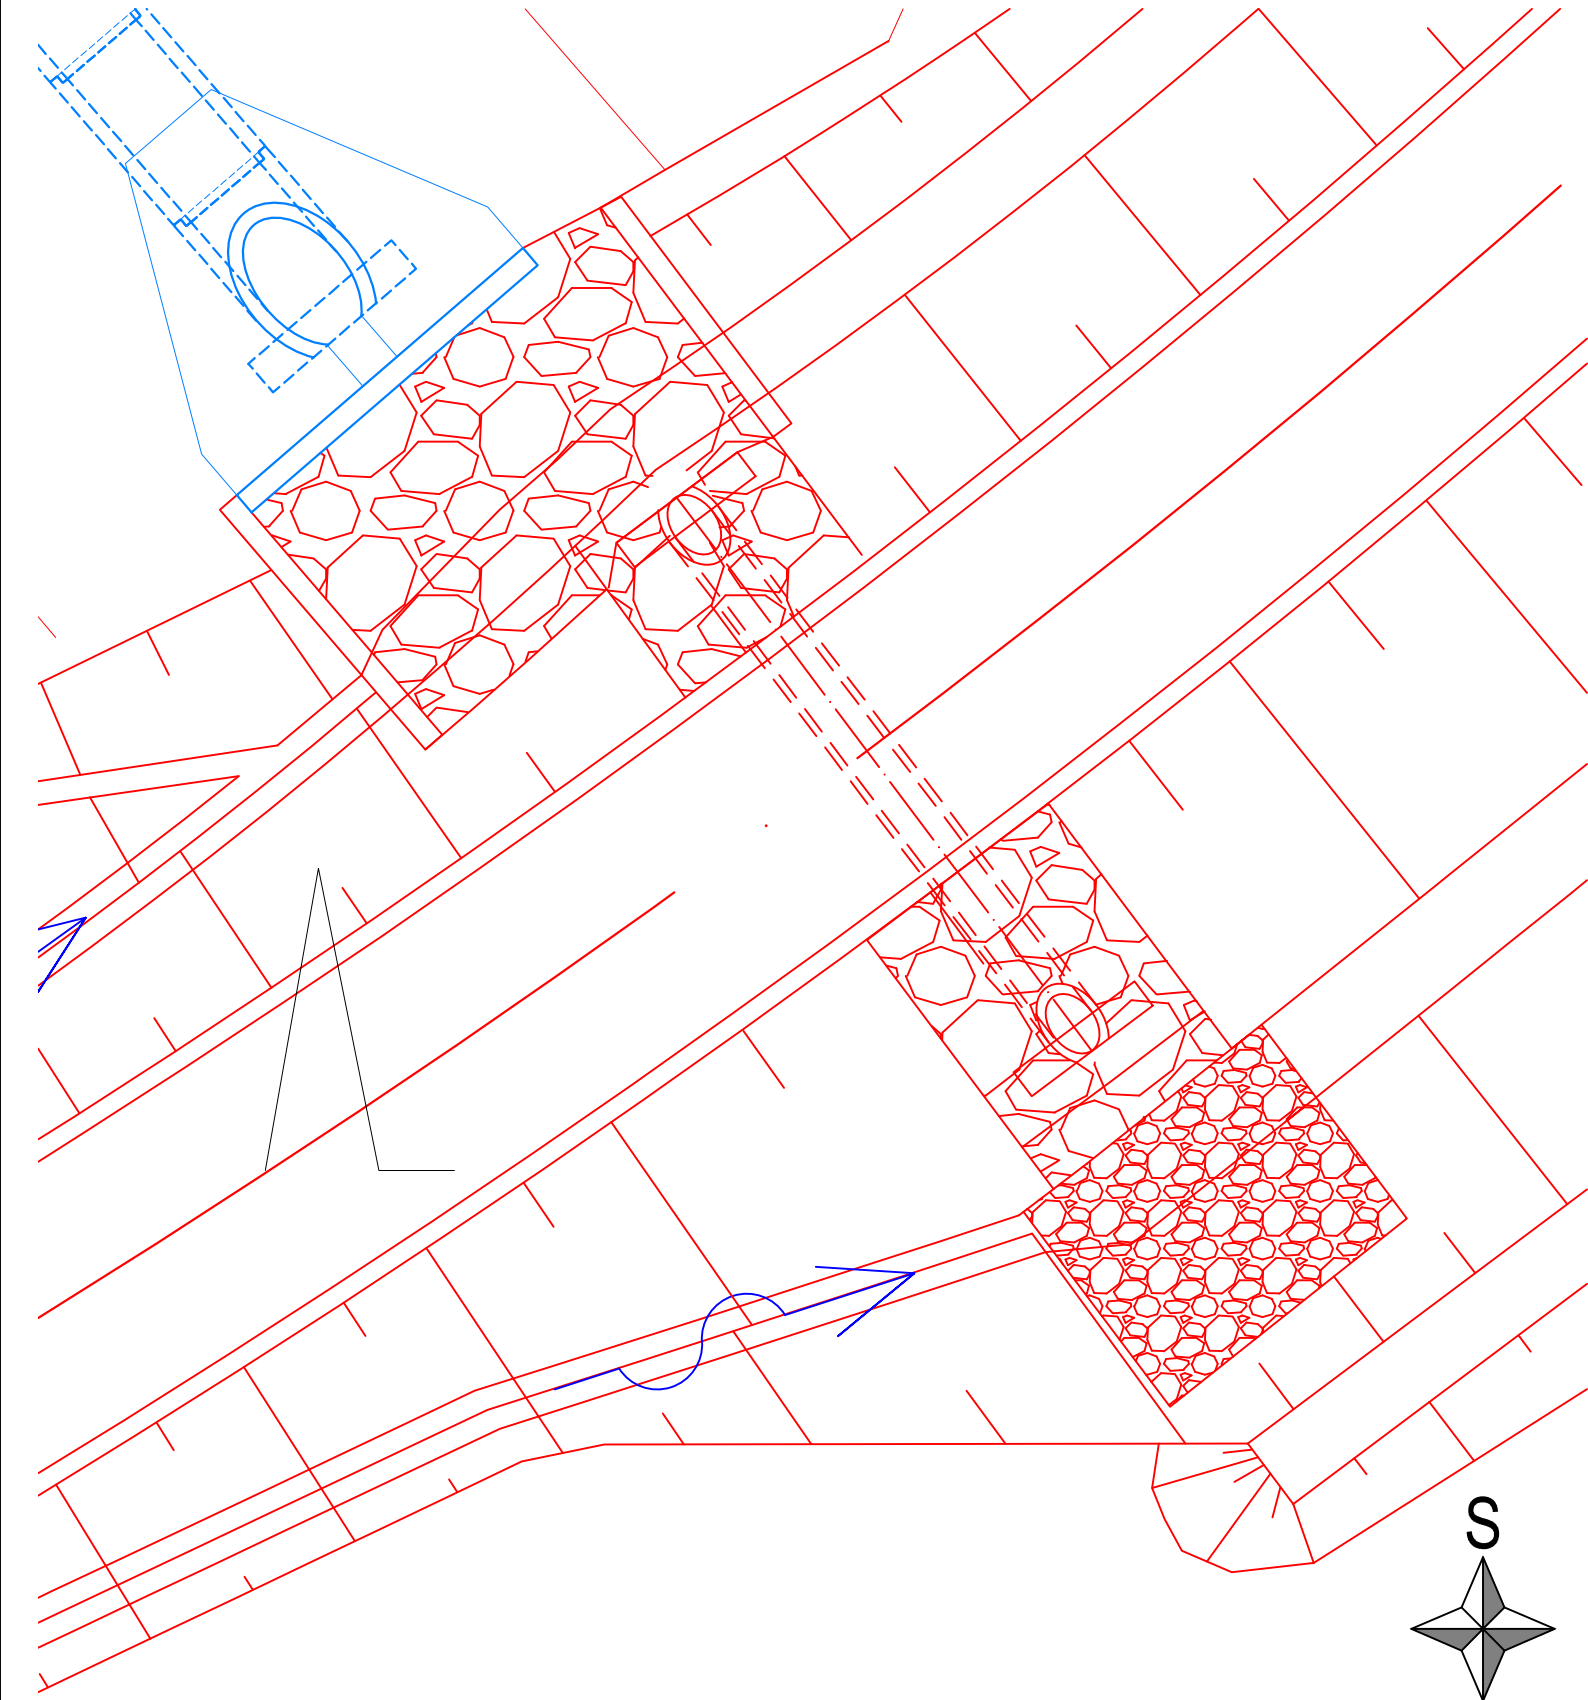

SO 161

D.1.1

VÝŠKOVÝ SYSTÉM Bpv

SOUŘADNICOVÝ SYSTÉM S-JTSK

Číslo změny:	Obsah změny:	Datum změny:
01	-	-
02	-	-
03	-	-

Objednatel:	Ředitelství silnic a dálnic s. p. Na Pankraci 546/56, 140 00 Praha 4
Stavbu zajišťuje Závod Praha Na Pankraci 546/56, 140 00 Praha 4	

Zhotovitel: Společníci ve sdružení	SG_Velké projekty BIM 2020 zastoupené
SUDOP PRAHA a.s. Hlavní inženýr projektu: Ing. Roman Petřík	Olšanská 1a, 130 80 Praha 3 telefon: +420 267 094 111
	
	

Správce:	SUDOP PRAHA a.s. Olšanská 1a, 130 80 Praha 3 tel.: +420 267 094 111 e-mail: praha@sudop.cz	Vedoucí týmu:	Asistent vedoucího týmu:
		ING. ROMAN PETŘÍK	ING. PAVEL MICHL
			Specialista profese:
			-

Zpracovatel částí:	projektová, průzkumná a konzultační společnost PUDIS a.s., Podbabská 1014/20, 160 00 Praha 6 tel.: +420 267 004 111, www.pudis.cz, info@pudis.cz
	

Vedoucí střediska:	Odpovědný projektant SO, IO, PS:	Vypracoval:	Kontroloval:
ING. ZDEŇKA BOLEHOVSKÁ	ING. MICHAL TUREK	ING. TOMÁŠ VÁŇA	ING. MICHAL TUREK

Název akce:	Číslo smlouvy:
	22-014.250
D11 1108 Jaroměř - Trutnov VD-ZDS + TP + AD	Projektový stupeň:
	VD-ZDS
Část:	Datum:
D.1.1 OBJEKTY POZEMNÍCH KOMUNIKACÍ VČETNĚ PROPUSTKŮ SO 161 PŘÍSTUPY NA POZEMKY V K.Ú BRUSNICE	11/2024
Název přílohy:	Číslo části:
	D.1.1
	Měřítko:
	1:100
	Počet formátů:
	4xA4
PROPUSTEK DN 800 V KM 0,822	Číslo přílohy:
	6.2

DOKUMENT LZE UŽÍVAT POUZE VE SMYSLU PŘÍSLUŠNÉ SMLOUVY O DÍLO. ŽÁDNÁ JEHO ČÁST NEMŮŽE BYT DLE ZÁKONA č. 121/2000 Sb. KOPIROVÁNA NEBO JINÝM ZPŮSOBEM ROZŠÍŘOVÁNA. BEZ SOUHLASU SUDOP PRAHA a.s.